


MILK PASTEURIZER 10 KLPH

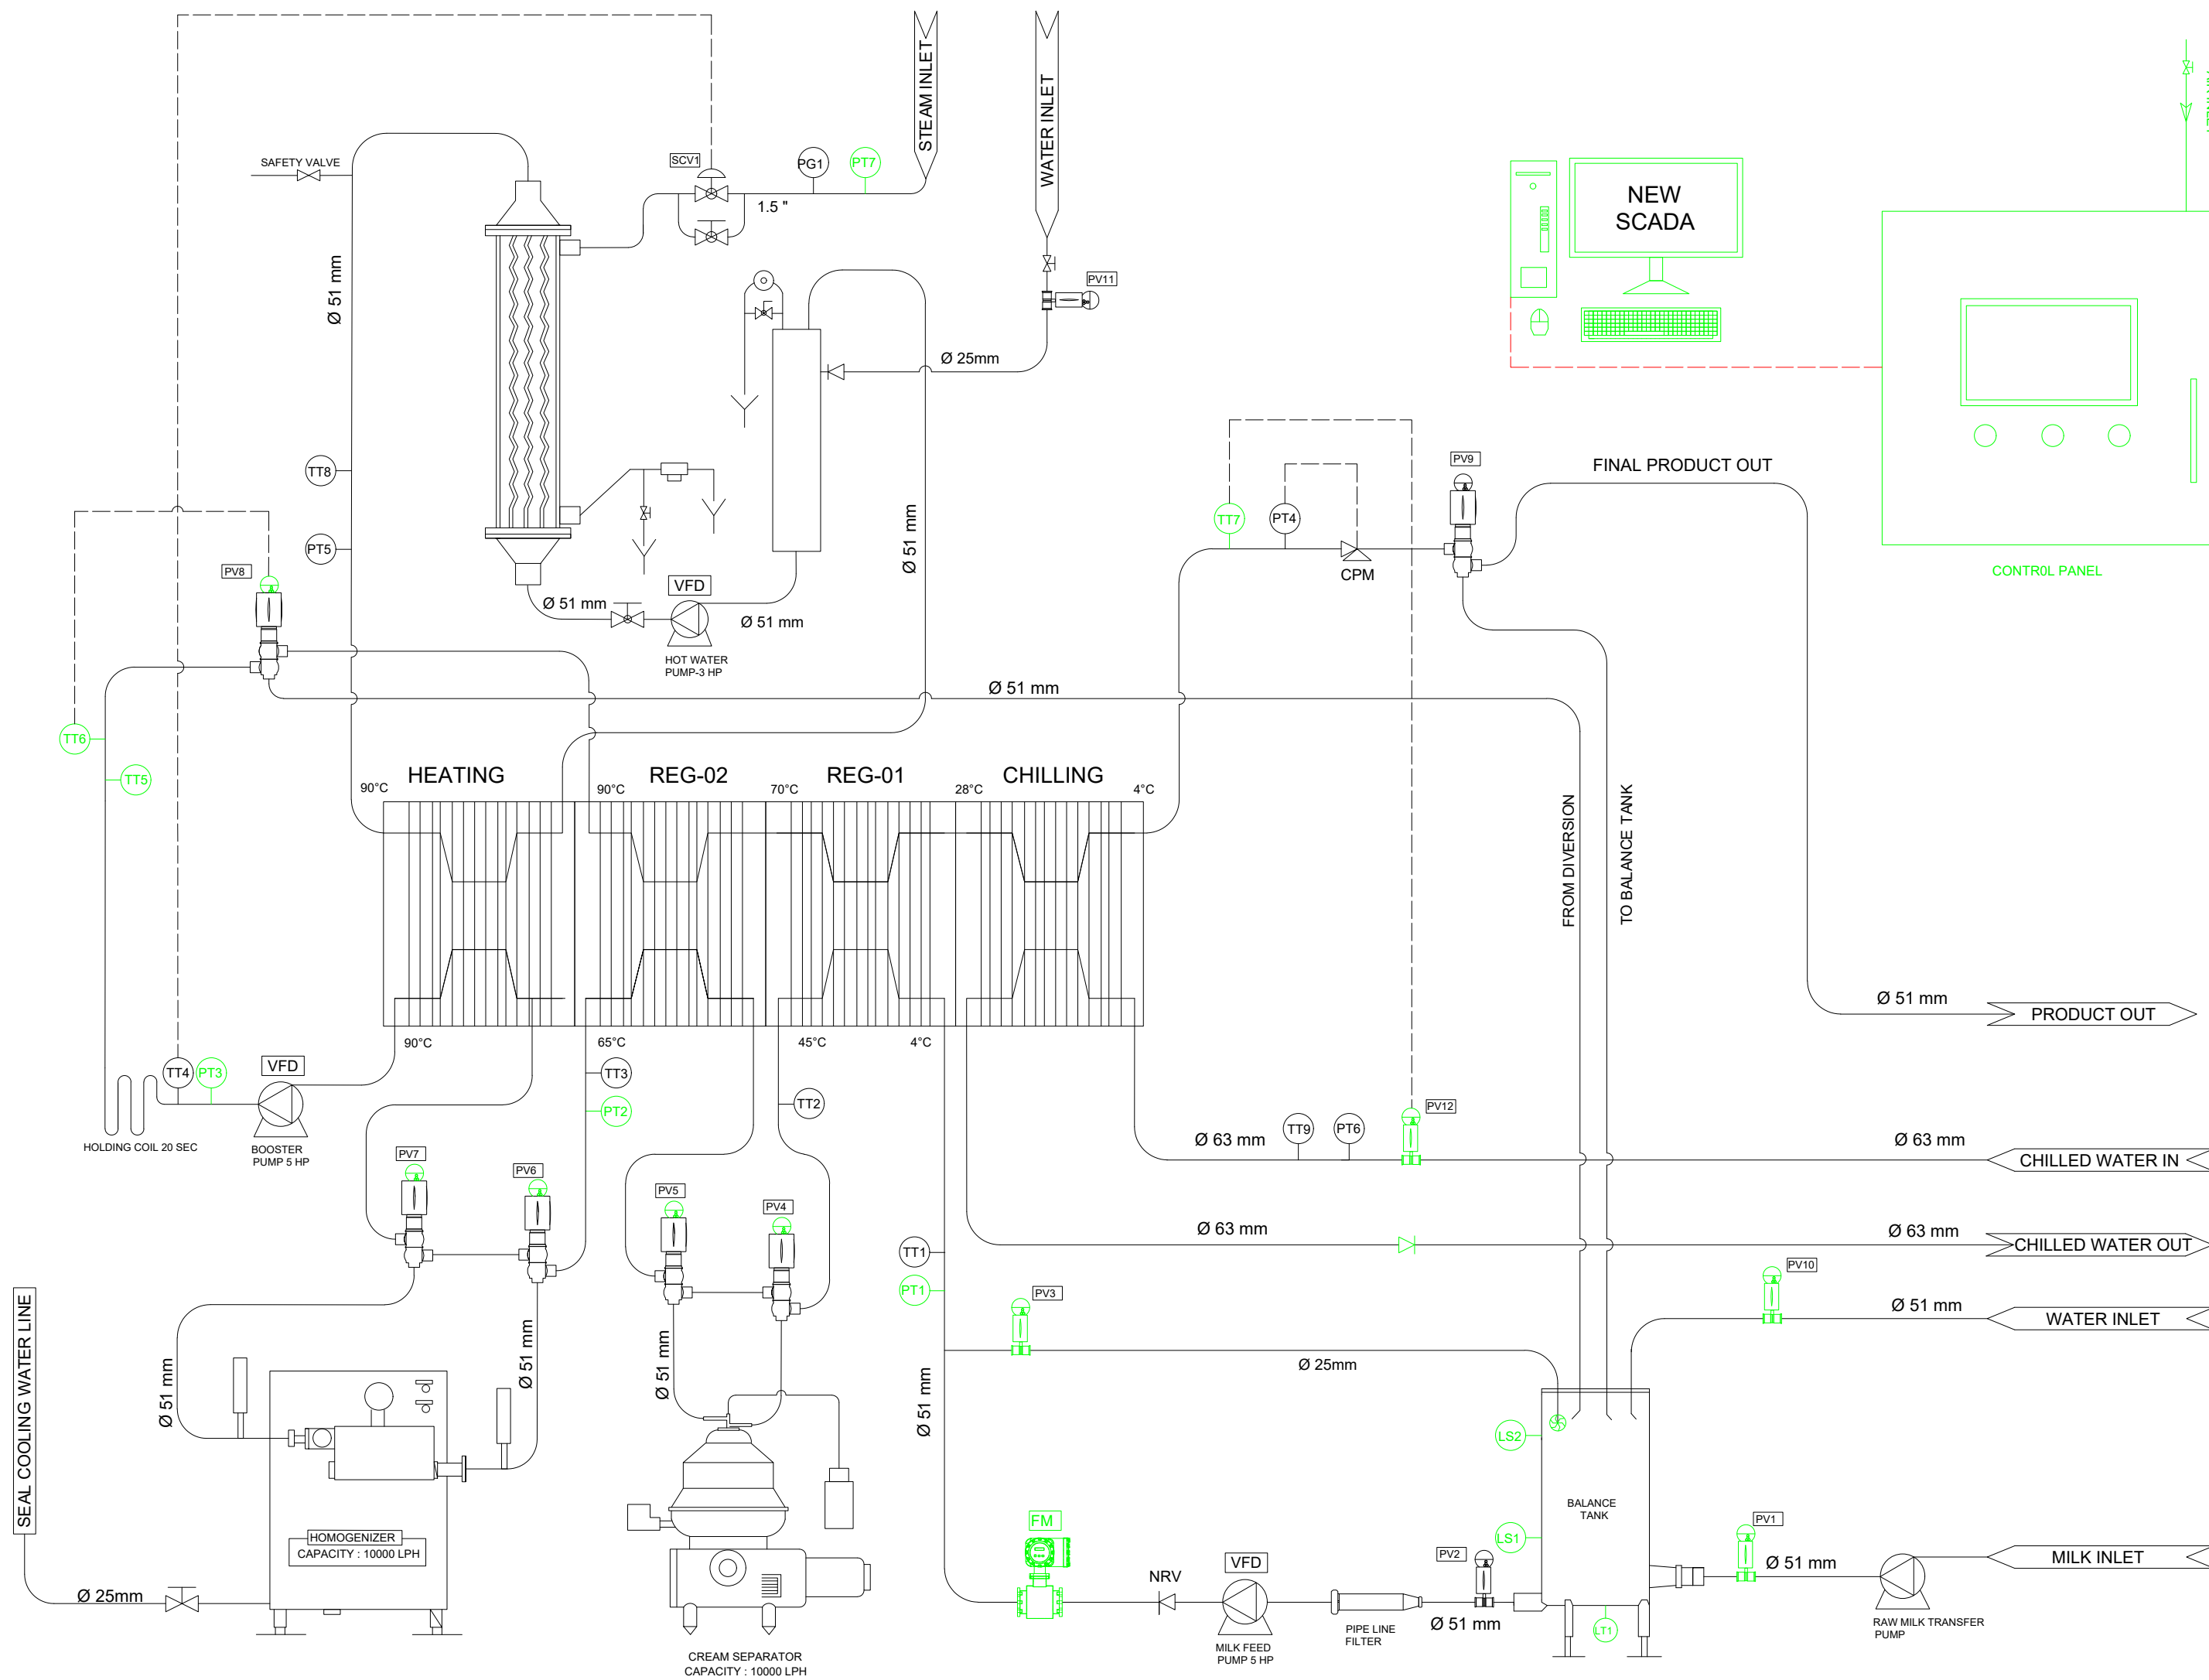

The design and drawing is not given or sold but loaned.
It remains the property of GOOSE INDUSTRIAL SOLUTIONS and subject to their recall.
It is confidential and must not be made public or copied or reproduced without previous written permission.



GOOSE INDUSTRIAL SOLUTIONS
PUNE

CLIENT : LACTALIS, BHOPAL

TITLE : MILK PASTEURIZER 10 KLPH P&ID

DRAWING NO : GP-LACTALIS, BHOPAL-PID-PSTRZ-001

DRAWN	AM	24.06.26	PROJECTION	SCALE	SHEET	REV.	SIZE
CHECKED	KD	24.06.26	-	NTS	1 OF 1	0	A2
APPROVED	JT	24.06.26					

REV.	DATE	REVISION DESCRIPTION	REV. BY	CHK. BY	APP. BY